



Company
Profile





Contents

Introduction.	1.0
Lighting Solution System.	2.0
Project Life Cycle.	3.0
Business Partners.	4.0
Selected Projects References.	5.0
Contact Details.	6.0



Symphonies in Light

1.0 Introduction

DAMAS LIGHTING LLC has been established in 2011 to answer the need of the on-growing market for high quality of European Light Fittings / Design and Supply of the blooming Gulf and UAE market.

Today, **DAMAS LIGHTING LLC**. has grown into one of the leading companies in the Light Fittings - Design and Supply, and prides itself in offering complete service to its clients, great variety of products and customized Lighting solutions of the highest quality that meets the needs of our clients and their projects.

With creative styles made by lighting designers worldwide, the most up to date trends and fashion styles and yet keeping the traditional way of international cultures, all of which are needed in a constantly evolving market,

DAMAS LIGHTING LLC. managed to offer ideas to create the perfect lighting solutions that suits every client needs.

DAMAS LIGHTING LLC. Partnered with a host of leading lightings manufacturers, the company succeeded in providing creative products that combines traditional and modern design, convenience, functionality and high quality with a guarantee that all products in the selection have been tried and tested to fulfill its maximum function.

DAMAS LIGHTING LLC. stands by its mission: Quality, Service and Affordability with a credo of providing the complete Lighting solutions for the need of every individual client.



Light is Life

1.0 Introduction

Light is vital for everyone, for all our many activities and our safety. The right light makes all the difference to our comfort.

Light helps to create ambience and atmosphere, in short ***Light is Life***.

We are, in **DAMAS LIGHTING** LLC. interested in developing lighting solutions that are ideal to the specific requirements of prestigious projects, And create lighting schemes in harmony with the infrastructure projects you undertake.



We are committed to give clients all their needs in what concerns lighting solutions. And we are able to generate a return on your investment by adding value to your projects through the delivery of unique and fully customized lighting solutions.

DAMAS LIGHTING LLC. offers the required Technical and ***Design*** study for unique projects, and supplies virtually all types of European light fixtures from decorative indoor and outdoor/ Façade- Landscape luminaries, to the most sophisticated and up-to-date technology.

DAMAS LIGHTING LLC. has a prestigious clients such as: Their Highnesses Sheikhs (Projects & Palaces), Representatives of the Business Community, Reputed Interior Designers and Architects for several Projects as Malls, Hotels, Palaces, Residences....etc.

With highest standard of quality and affordability:

- Intelligent Lighting, LED Technology, Optical Fibre & SOLAR Lighting.
- Interior Fixtures: Ceiling, Wall & Floor/ Recessed, Surface, Suspension.
- Residential Amenities: Wall Lights, Bollards, Step Lights & Buried Lights.
- Exterior Floodlight: Façade, Olympic, Tunnels & Underpass.
- Underwater, Swimming Pool, and Fountains Lighting.
- ATEX- Atmosphere Explosive/ Water-Proof Fixture.
- Batten, Track & Rapid Lighting System.
- Commercial & Industrial High-Bays.
- Airports Lighting & Aviation Light.
- Street Lighting with poles.
- Post-top Amenities.
- Hospital Lighting.
- Classic Lighting.
- Emergency Light.

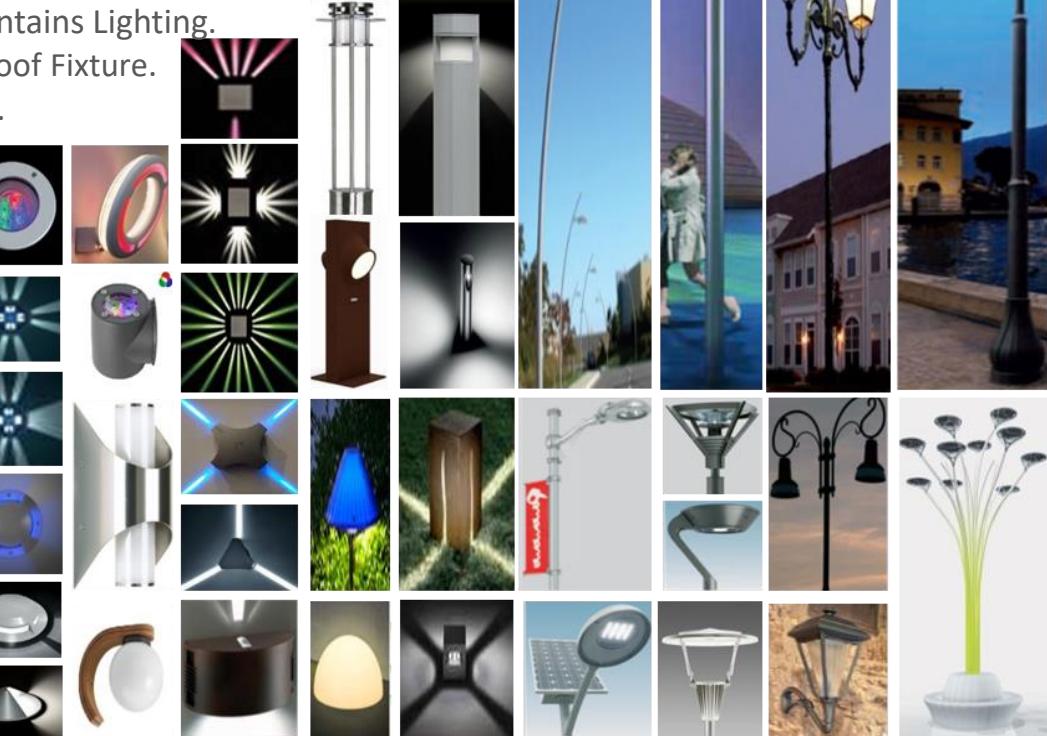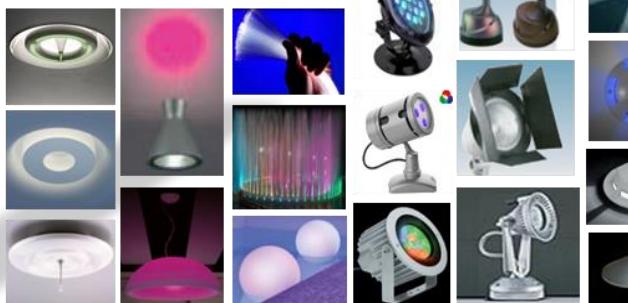


Decorative Lighting.

2.0 Lighting Solution System



3.0 Project life Cycle

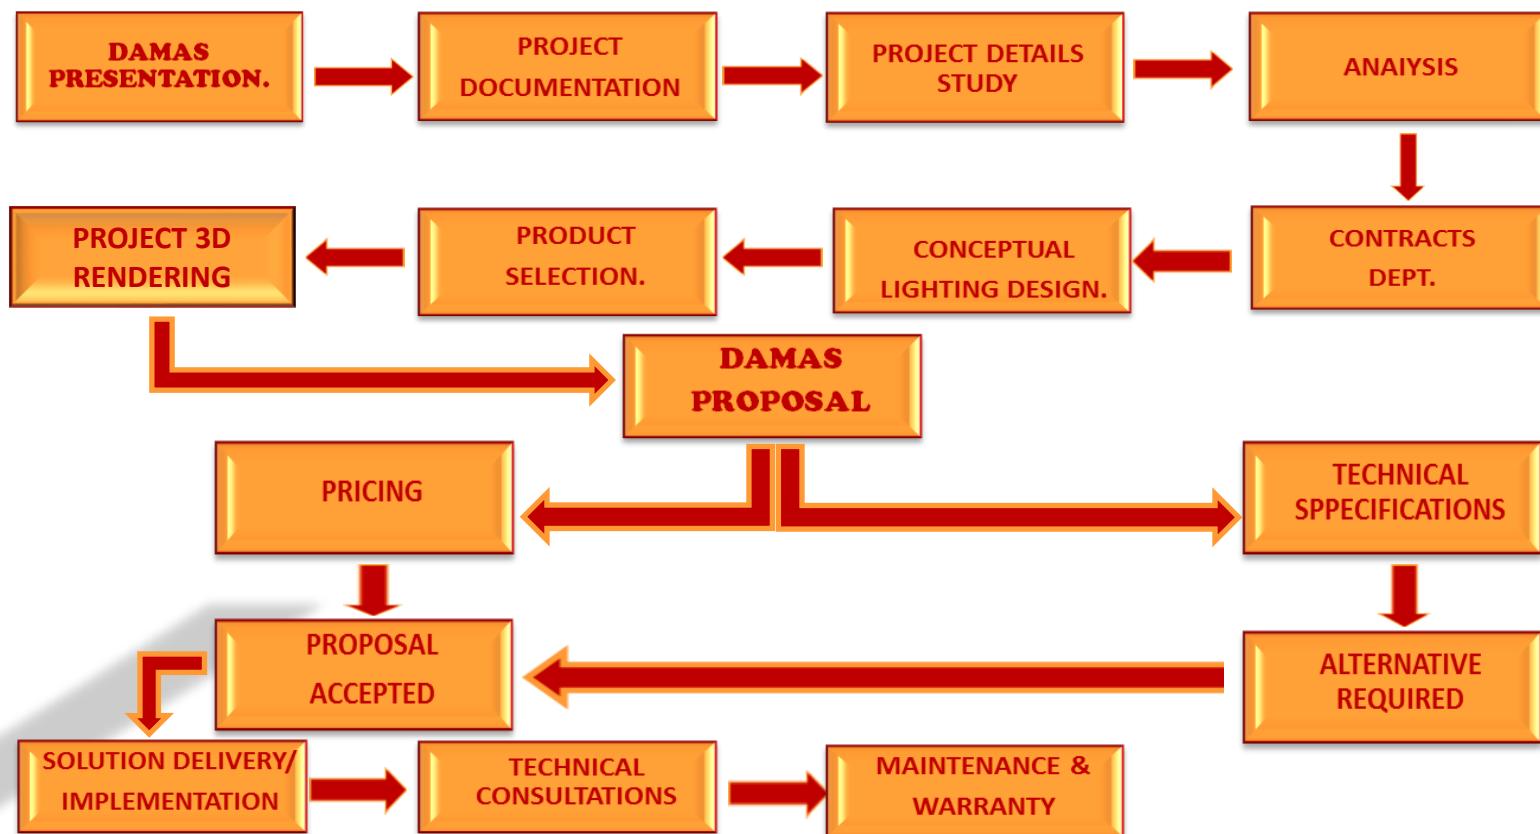



4.0 Business Partners

We are strategic partner to **DISANO ILLUMINAZIONE GROUP**- the largest and best lighting factory in ITALY - established and based in MILANO since 1957.

We are also one of the leading providers of innovative lighting imported EUROPE, USA, CANADA and AUSTRALIA.

We have built a powerful tie-up with many international brands such as:







Private Palace for Sheikha Shamsa Bint Suhail Al Mazroui wife of UAE President H.H. Sheikh Khalifa Bin Zayed Al Nahyan in DUBAI- Jumairah.



Private Villas for Sheikh Butti Bin Jumaa Al Maktoum in Umm Al Quwain.



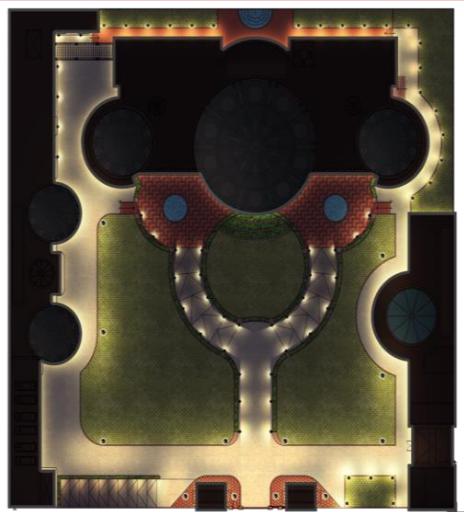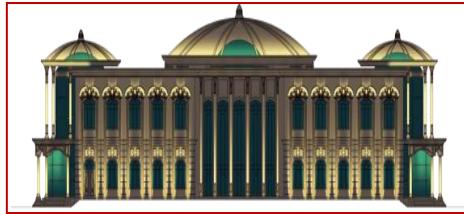

PRIVATE PALACE in AL-KHWANEEJ at DUBAI.

CIVIL DEFENSE BUILDING OPTION 1

FACADE LIGHTING DESIGN

Fosnova disano

d
damasLIGHTING
CREATIVE TECHNOLOGY

1 SURFACE MOUNTED LINEAR WALLWASHER LED LIGHT FOSNOVA LISET IP65 -LED 12X1.1W AT 1,215MM LENGTH -LED 6X1.1W AT 615MM LENGTH

2 SURFACE MOUNTED SQUARE LED LIGHT DISANO 1848 RIQUADRO LED -LED 15W

3 SURFACE MOUNTED LINEAR LED LIGHT FOSNOVA MICROLISET IP65 -LED 72X0.2W AT 1,235MM LENGTH -LED 56X0.2W AT 935MM LENGTH LED 36X0.2W AT 635MM LENGTH

4 RECESSED MOUNTED LED ADJUSTABLE UPLIGHT DISANO 1678 FLOOR -LED ES -LED 16W

5 RECESSED MOUNTED LED LINEAR FLOODLIGHT DISANO 1837 SICURA -ELLiptical LED -LED 56W AT 1,230MM LENGTH



Façade Lighting Design/ Directorate General of Civil Defense - DUBAI


5.0 Selected Project References.







RENDERED NIGHT-SHOT PERSPECTIVE (ANIMATION)

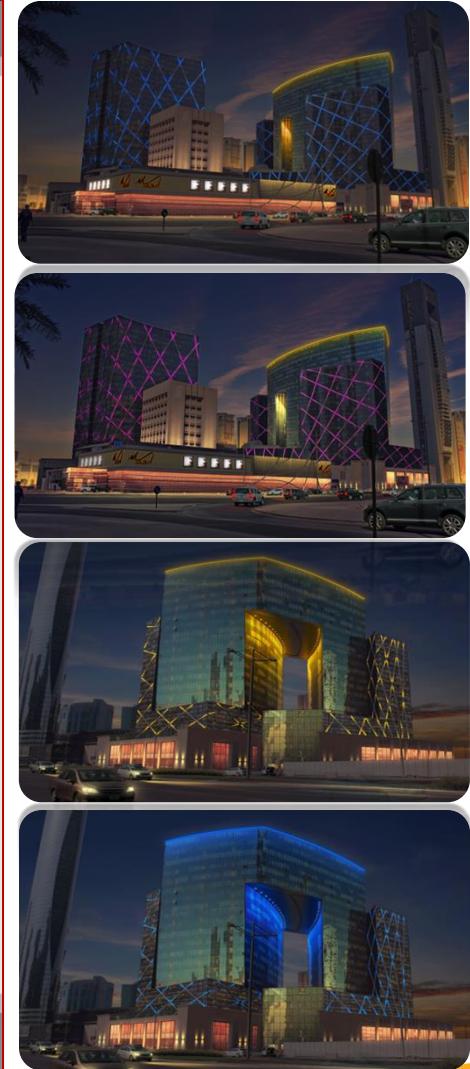



AL-FUJAIRAH MALL PROJECT - LULU HYPERMARKET .

disano Fosnova



AL-FUJAIRAH MALL PROJECT

disano Fosnova




DAY -TIME



Mosque in Al Quoz 2nd At DUBAI

NIGHT -TIME

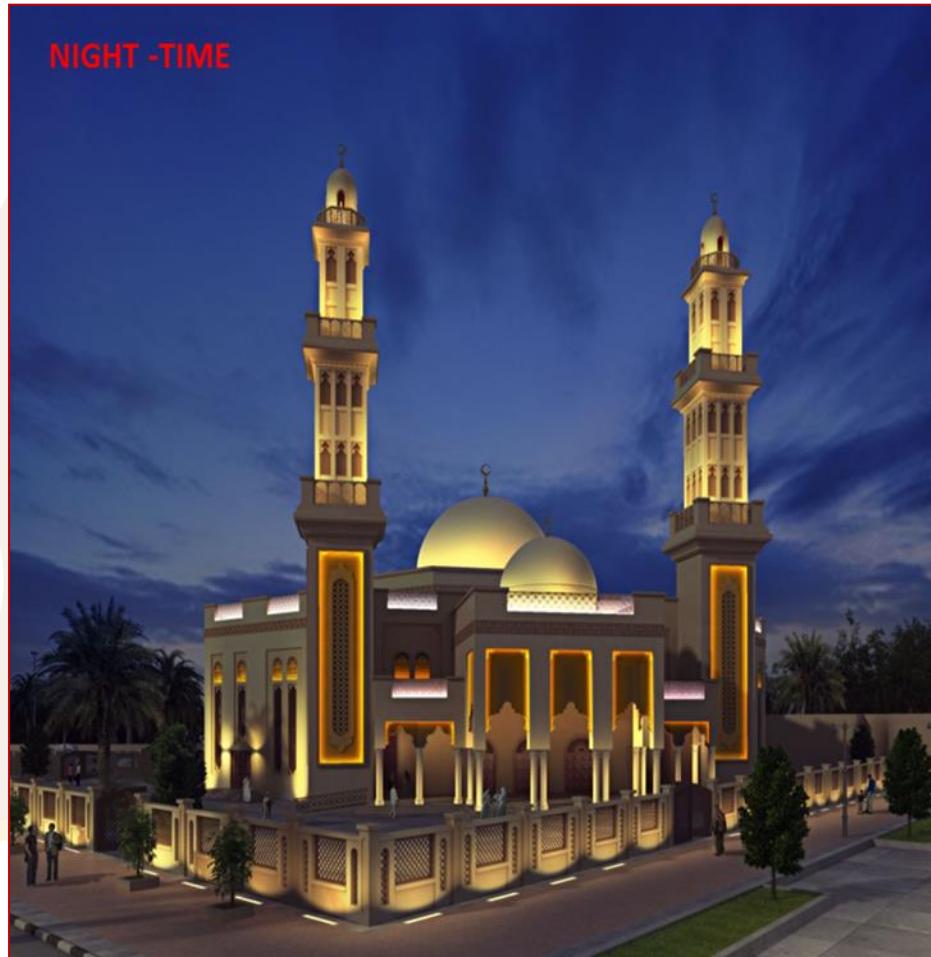



FACADE LIGHTING



DAY-SHOT PERSPECTIVE
SCALE NTS



NIGHT-SHOT PERSPECTIVE
SCALE NTS

FIXTURES




DIGANO 1528 ELFO
SURFACE MOUNTED ADJUSTABLE FLOODLIGHT
- CDM-T 150W



DISANO 1525 ELFO
SURFACE MOUNTED ADJUSTABLE FLOODLIGHT
- CDM-T 70W



DISANO 1536 KOALA
SURFACE MOUNTED ADJUSTABLE MINI FLOODLIGHT
- CDM-TM 35W

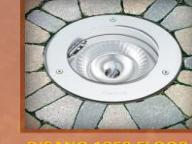

DISANO 1858 FLOOR
RECESSED FLOOR MOUNTED ADJUSTABLE UPLIGHT
- CDM-T 70W



FOSNOVA L1SET IP
SURFACE MOUNTED LINEAR WALLWASHER LIGHT
- 6.6W @ 615mm LENGTH
- 13.2W @ 1215mm LENGTH



DISANO 1856 FLOOR
RECESSED GROUND MOUNTED UPLIGHT
- CDM-T 35W



FOSNOVA MICROLISSET
LINEAR LED LIGHT
- 54x0.3W LED @ 935mm LENGTH

HOTEL PROJECT in Al Muraqqabt At DUBAI

Fosnova disano www.fosnova.com

FACADE LIGHTING



HOTEL PROJECT

FIXTURES



DISANO 1528 ELFO
SURFACE MOUNTED ADJUSTABLE FLOODLIGHT
- CDM-T 150W



FOSNOVA LISET IP
SURFACE MOUNTED LINEAR WALLWASHER LIGHT
- 6.6W @ 615mm LENGTH
- 13.2W @ 1215mm LENGTH



DISANO 1525 ELFO
SURFACE MOUNTED ADJUSTABLE FLOODLIGHT
- CDM-T 70W



DISANO 1856 FLOOR
RECESSED GROUND MOUNTED UPLIGHT
- CDM-T 35W



DISANO 1536 KOALA
SURFACE MOUNTED ADJUSTABLE MINI FLOODLIGHT
- CDM-TM 35W



FOSNOVA MICROLISSET
LINEAR LED LIGHT
- 54x0.3W LED @ 935mm LENGTH



DISANO 1858 FLOOR
RECESSED FLOOR MOUNTED ADJUSTABLE UPLIGHT
- CDM-T 70W

Fosnova disano www.fosnova.com

FACADE LIGHTING



FRONT ELEVATION
SCALE NTS



LEFT SIDE ELEVATION
SCALE NTS



RIGHT ELEVATION
SCALE NTS



RIGHT SIDE ELEVATION
SCALE NTS

HOTEL PROJECT

FIXTURES



DISANO 1528 ELFO
SURFACE MOUNTED ADJUSTABLE FLOODLIGHT
- CDM-T 150W



DISANO 1525 ELFO
SURFACE MOUNTED ADJUSTABLE FLOODLIGHT
- CDM-T 70W



DISANO 1536 KOALA
SURFACE MOUNTED ADJUSTABLE
MINI FLOODLIGHT
- CDM-TM 35W



DISANO 1554 CLESSIDRA
SURFACE MOUNTED LED LIGHT
- 2xPOWERLED 3.3W +
2xPOWERLED 3.3W



DISANO 1547 CLESSIDRA
SURFACE MOUNTED WALL
LIGHT
- 2 x FLC-EL 23W



DISANO 1856 FLOOR
RECESSED GROUND MOUNTED
UPLIGHT
- CDM-T 35W



FOSNOVA MICROLISSET
LINEAR LED LIGHT
- 54x0.3W LED @ 935mm LENGTH

Fosnova disano
Bridging Light

FACADE LIGHTING



DAY-SHOT PERSPECTIVE
SCALE NTS



NIGHT-SHOT PERSPECTIVE
SCALE NTS

CORNICA RESIDENTIAL BUILDING in Sport City At DUBAI

FIXTURES



FOSNOVA MICROLISET IP
LINEAR LED LIGHT
- 18x0.3W LED AT 635mm LENGTH



DISANO 1547 CLESSIDRA 1
SURFACE MOUNTED WALL
LIGHT
- FLC-EL 2x23W



DISANO 1833 RODO
SURFACE MOUNTED
FLOODLIGHT
- HCL-T 400W



DISANO 1537 KOALA
SURFACE MOUNTED MINI
FLOODLIGHT
- LED 3.3W



DISANO 1646 MAXIFLOOR
RECESSED GROUND MOUNTED
UPLIGHT
- CDM-T 70W



DISANO 1544 GLOBO
SURFACE MOUNTED
DOWNLIGHT
- FLC 2x9W



DISANO 1525 ELFO
SURFACE MOUNTED
FLOODLIGHT
- CDM-T 70W




DISANO 1294 CILINDRO
SURFACE MOUNTED
DOWNLIGHT
- CDM-T 70W

Fosnova disano




FACADE LIGHTING

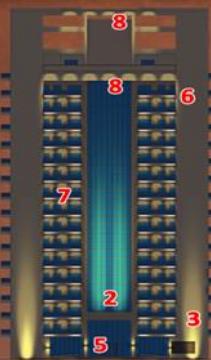


FRONT ELEVATION
SCALE NTS



REAR ELEVATION
SCALE NTS

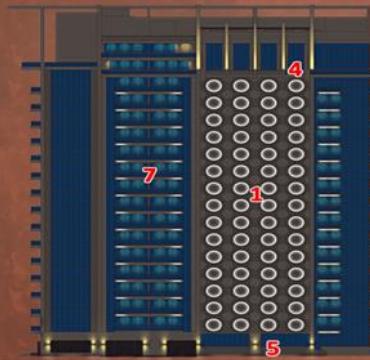

LEFT SIDE ELEVATION
SCALE NTS

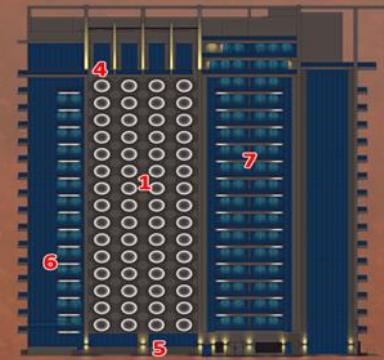

RIGHT SIDE ELEVATION
SCALE NTS

CORNICA RESIDENTIAL BUILDING

FIXTURES



FOSNOVA MICROLISET IP
LINEAR LED LIGHT
- 18x0.3W LED AT 635mm LENGTH



DISANO 1547 CLESSIDRA 1
SURFACE MOUNTED WALL
LIGHT
- FLC-EL 2x23W



DISANO 1833 RODO
SURFACE MOUNTED
FLOODLIGHT
- HCI-T 400W



DISANO 1537 KOALA
SURFACE MOUNTED MINI
FLOODLIGHT
- LED 3.3W



DISANO 1646 MAXIFLOOR
RECESSED GROUND MOUNTED
UPLIGHTER
- CDM-T 70W



DISANO 1544 GLOBO
SURFACE MOUNTED
DOWNLIGHT
- FLC 2x9W



DISANO 1525 ELFO
SURFACE MOUNTED
FLOODLIGHT
- CDM-T 70W



DISANO 1294 CILANDRO
SURFACE MOUNTED
DOWNLIGHT
- CDM-T 70W

Fosnova disano



6.0 Contact Details

DAMAS LIGHTING

Tel. +971 4 2398883.
Fax: +971 4 2398884.
E-mail: info@damaslighting.ae
Hamarain Center, Deira- DUBAI-UAE.

MANAGEMENT

E-mail: momen@damaslighting.ae

SALES DEPARTMENT

E-mail: sales@damaslighting.ae

TECHNICAL DEPARTMENT

E-mail: technical@damaslighting.ae

DESIGN DEPARTMENT

E-mail: design@damaslighting.ae

LOGISTIC DEPARTMENT

E-mail: damaslit@eim.ae

